


CONFIDENCIAL
Autorizada Filial

CONFIDENCIAL
Autorizada Filial

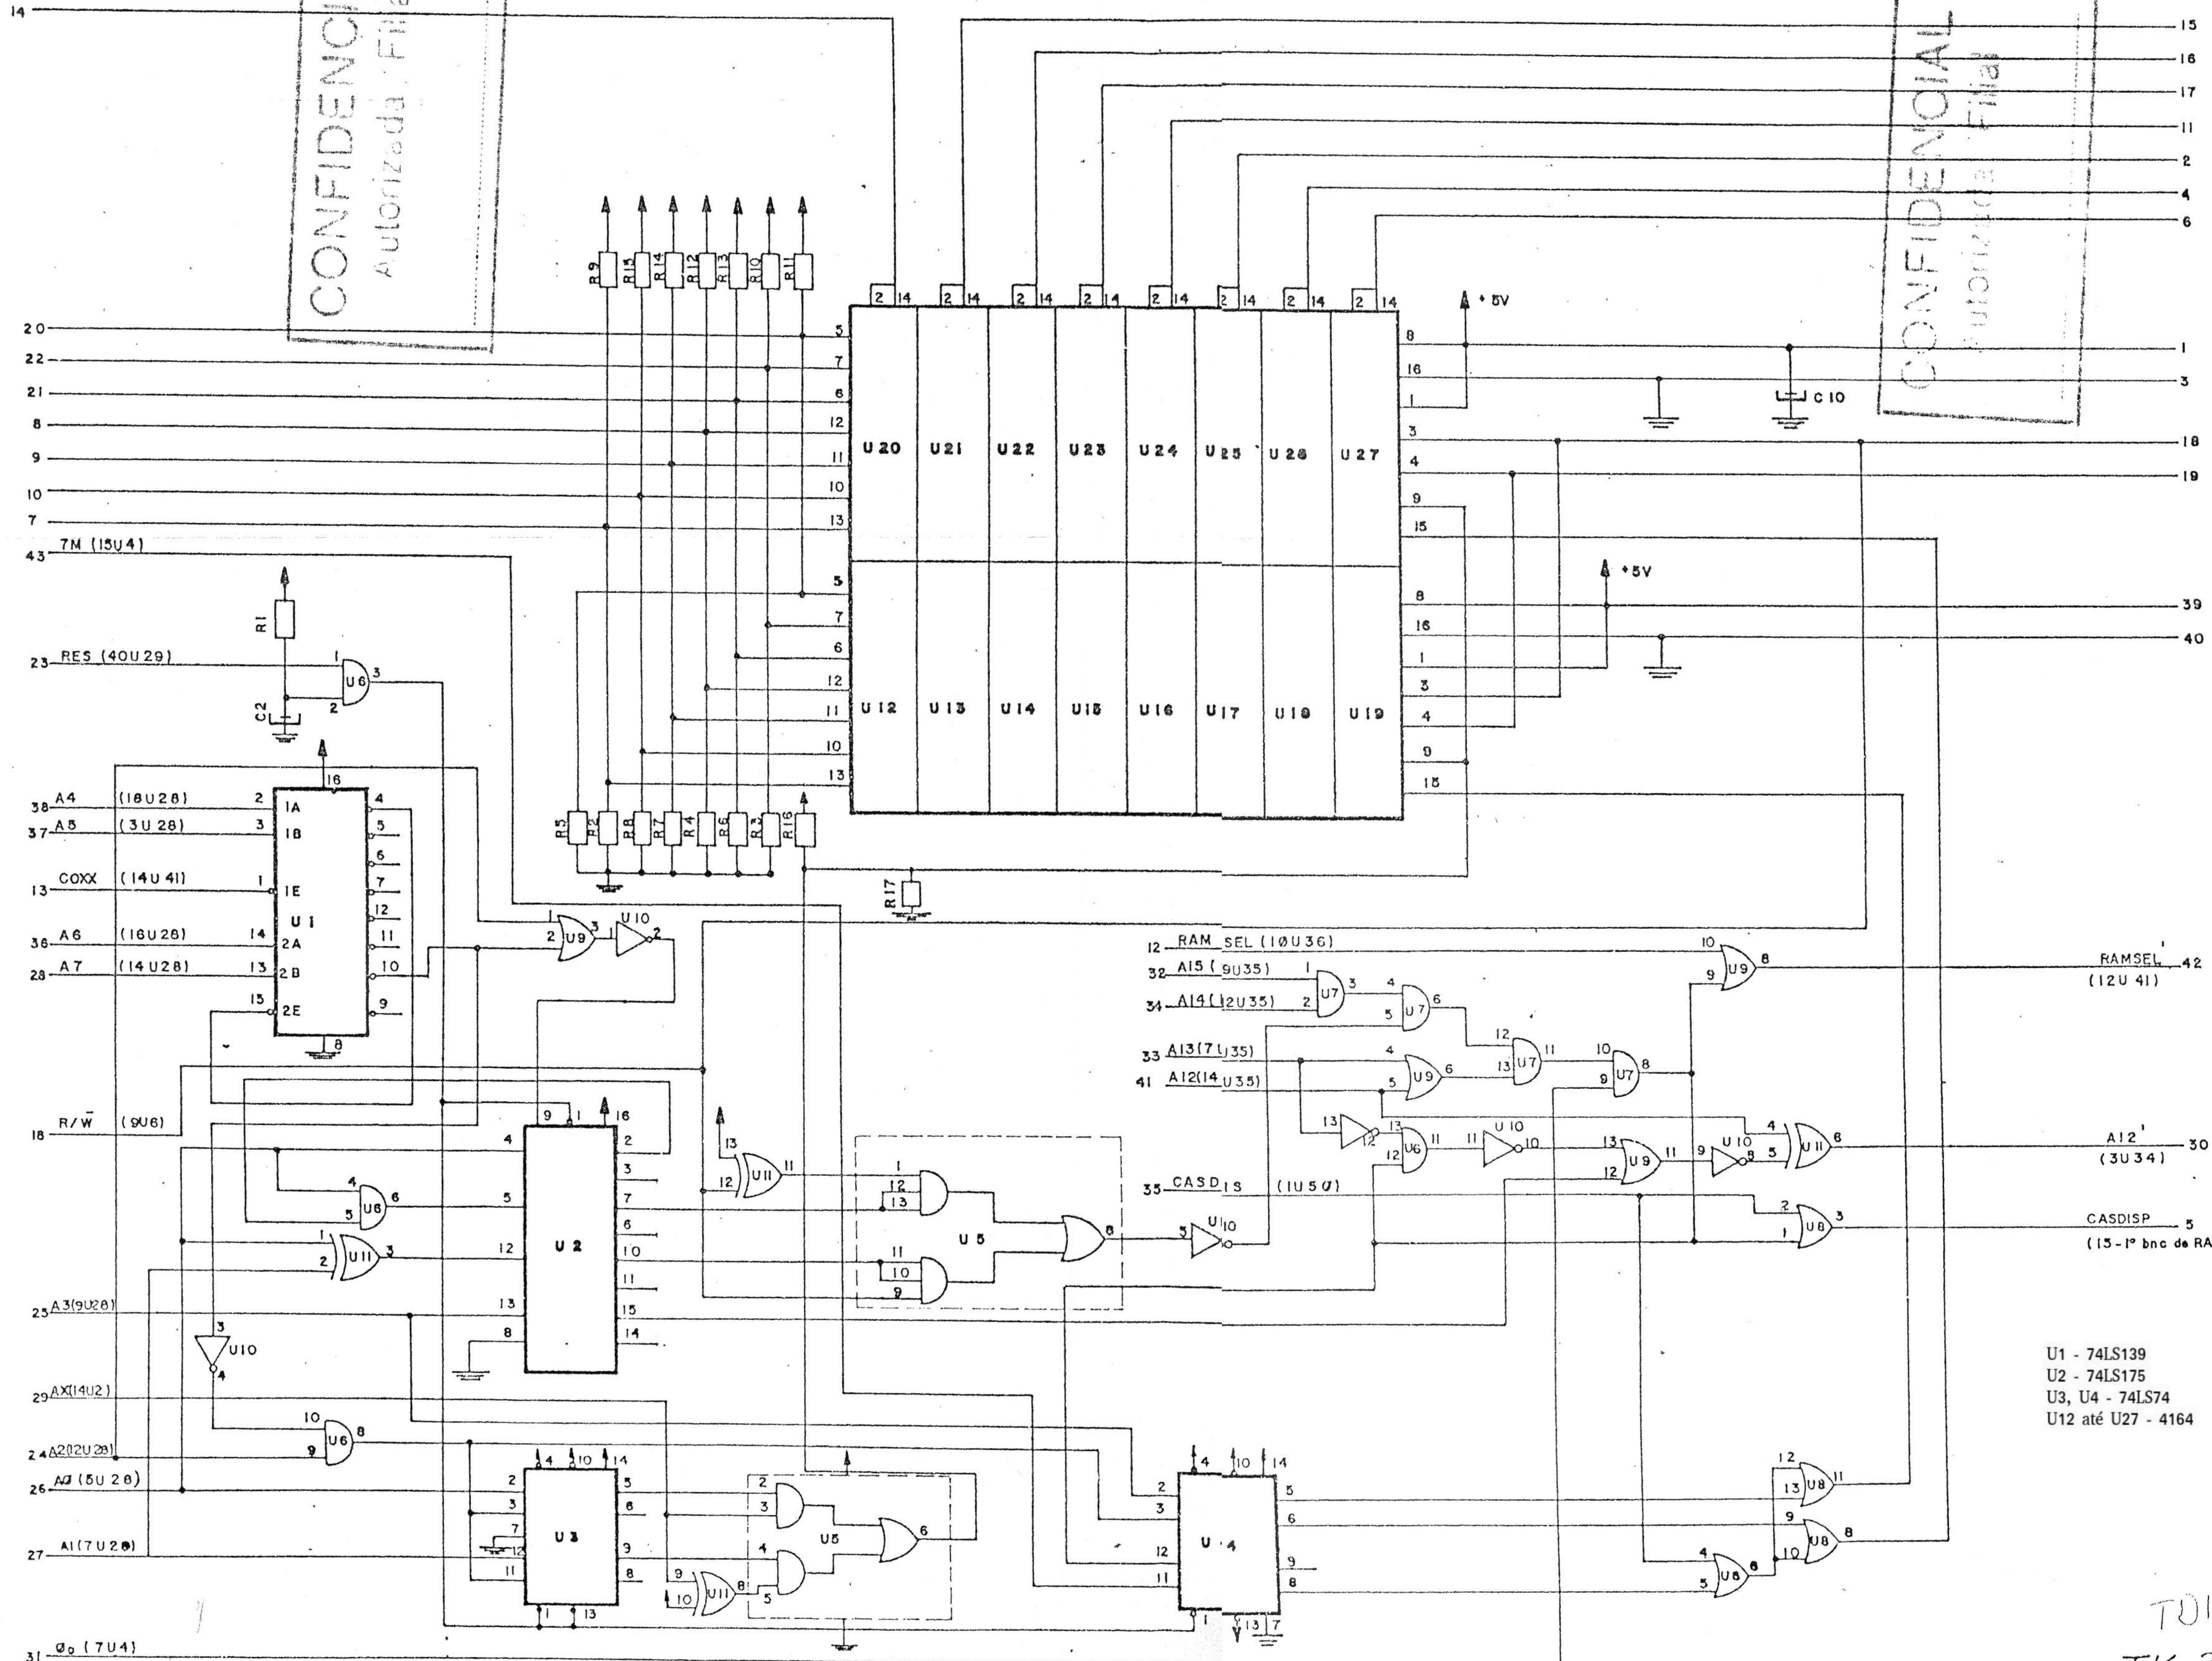

TD112
TK-2000
01/85